



MV JATI SEVEN

SFCB /UTILITIES VESSEL

General

Owners	: Dinastia Jati Sdn Bhd
IMO No.	: 9754197
Official Number	: 335668
Builder	: Strategic Marine (Singapore) Ltd.
Built	: 2014
Flag / Port of Registration	: Malaysia / Port Klang
Call sign	: 9MQI6
Classification	: Bureau Veritas (BV)

Dimension

Tonnage	- GT	: 288 T
	- NT	: 87 T
Length	- Overall	: 40.40 m
Beam	- Moulded	: 7.90 m
Depth		: 3.62 m
Draft		: 1.90 m

Capacities

Cargo Deck Space	: 120.00m ²
Strength	: 2 T/m ²
Reefer Point	: 4 nos on deck (50/440 VAC)
Portable Water Tanks	: 30 m ³
Fuel Oil Tanks	: 70 m ³
Lubrication Oil	: 800 litres
Cargo Weight.	- Maximum : Approx. 50 T
Deadweight.	- Maximum : TBA
	- Light displacement : TBA

Propulsion

Main Engine	- Type	: 3 x Cummins KTA38M2 Tier 2
	- BHP	: 3 x 1350 BHP @ 1900 RPM Total: 4050 BHP
Propellers		: 3 x Fixed Pitch Propeller (FPP)
Bow Thruster		: 2 MT lateral thrust
Controls		: 2 control stands
Starter		: Electrical
Reduction Gear & Ratio		: Twin Disc, MG 6690 & 6848 SC, 2.47:1
Speed / Consumption - Maximum ltr/hr		: 28.7 Knots @ 100% / Approx 762.5 ltr/hr
	- Cruising	: 26.8 knots @ 85% MCR/Approx 666 ltr/hr
	- Genset	: Approx 25 ltr/hr
Generators	- Type	: 2 x CUMMINS BT 5.9 D(M)
	- kW	: 2 x 80 kW
	- Voltage	: 415 V
	- Phase	: 3 phases
	- Hz	: 50 Hz

Accommodation

Cabin/ Berth	: 9 nos / 15 units (2 berths x 6 nos) (1 berths x 3 nos)
Crew	: 10 pax
Passengers	: 70 pax (Business Class inclined seat with individual hand rest, Fully Air- conditioning.

Life Saving Equipment

Water Curtain	: All around accommodation
Inflatable Life Rafts	: 25 men x 5 nos.
Rescue Boat	: 6 men x 1 Semi-Rigid rescue boat c/w 25hp outboard engine
Ring Buoys	: 8 nos
Man Over Board Marker	: 2 nos
Life Jackets / Work Vests	: 92 nos, (SOLAS approved) / 12 nos
SART	: 2 nos
EPIRB	: 1 no
Line Throwing Apparatus	: 1 set (4 projectiles & 4 lines)

Fire Fighting Equipment

Fire Extinguishers	: As per SOLAS
Fireman Outfit	: 1 nos
Breathing Apparatus	: 2 sets of SCBA

Navigation & Communication

As per SOLAS

Others

Bilge Pump / Ballast Pump	: 30 m ³ /hr @ 54 m head
Fire Pump	: 30 m ³ /hr @ 54 m head Fresh Water
Transfer Pump	: 13.5 m ³ /hr @ 55 m head
Fuel Transfer Pump	: 13.5 m ³ /hr @ 54 m head
Anchor Weight	: 255kg HHP
Anchor Windlass	: DOUBLE GYPSOY TWIN WARPING HEAD
Stove (cooker)	: 1 unit Electric 4 burner cook top
Dry Store	: 1 x 3.2 m ³
Fridge	: 1 x 2.7 m ³
Freezer	: 1 x 1.32 m ³
Washing machine	: 1 x 7kg
Dryer	: 1 x 7kg
Rescue Zone	: 2
Hospital / Owner Cabin	: 3

3A-6A, Jalan PJU 8/3A, Damansara


Perdana, 47820 Petaling Jaya,

Selangor, Malaysia.



+603 7722 3842

chartering@dinastijati.com





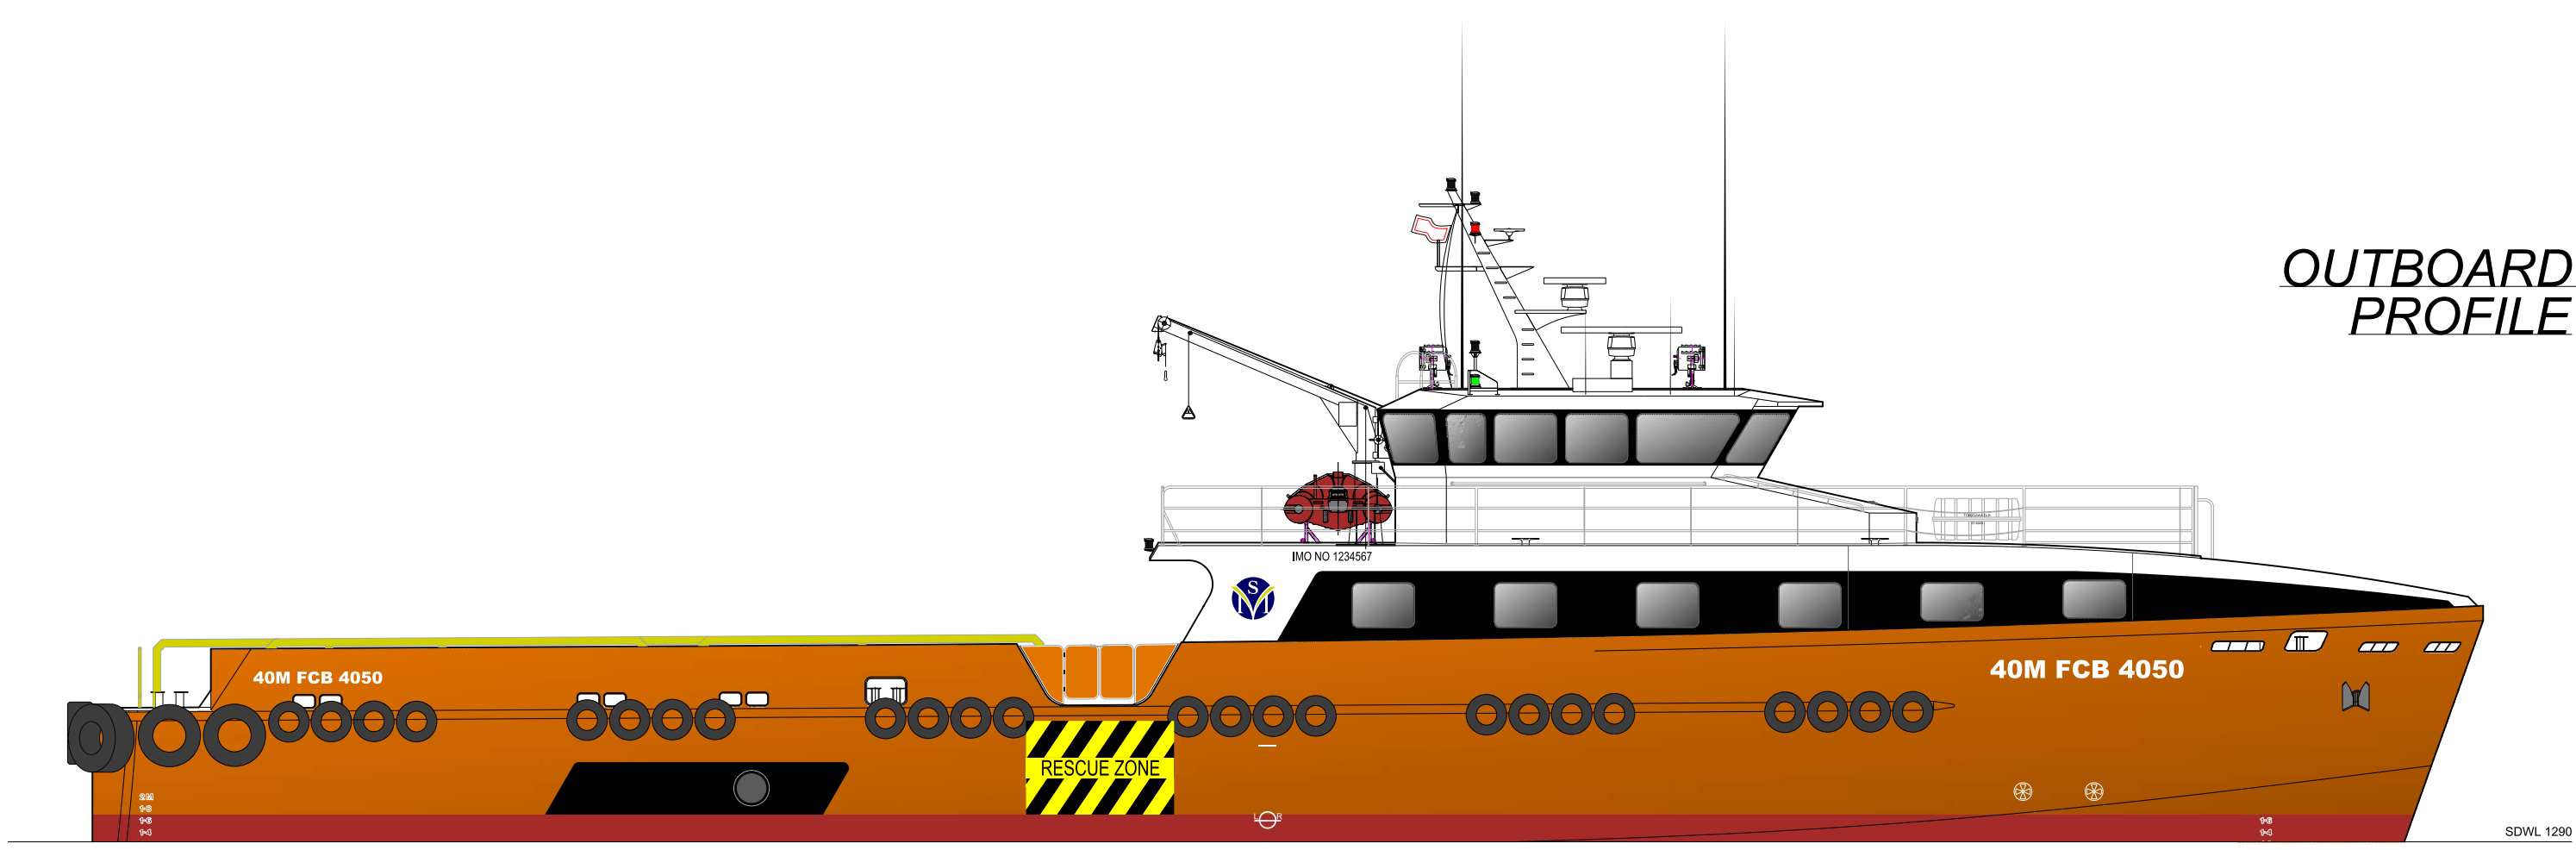

OUTBOARD
PROFILE

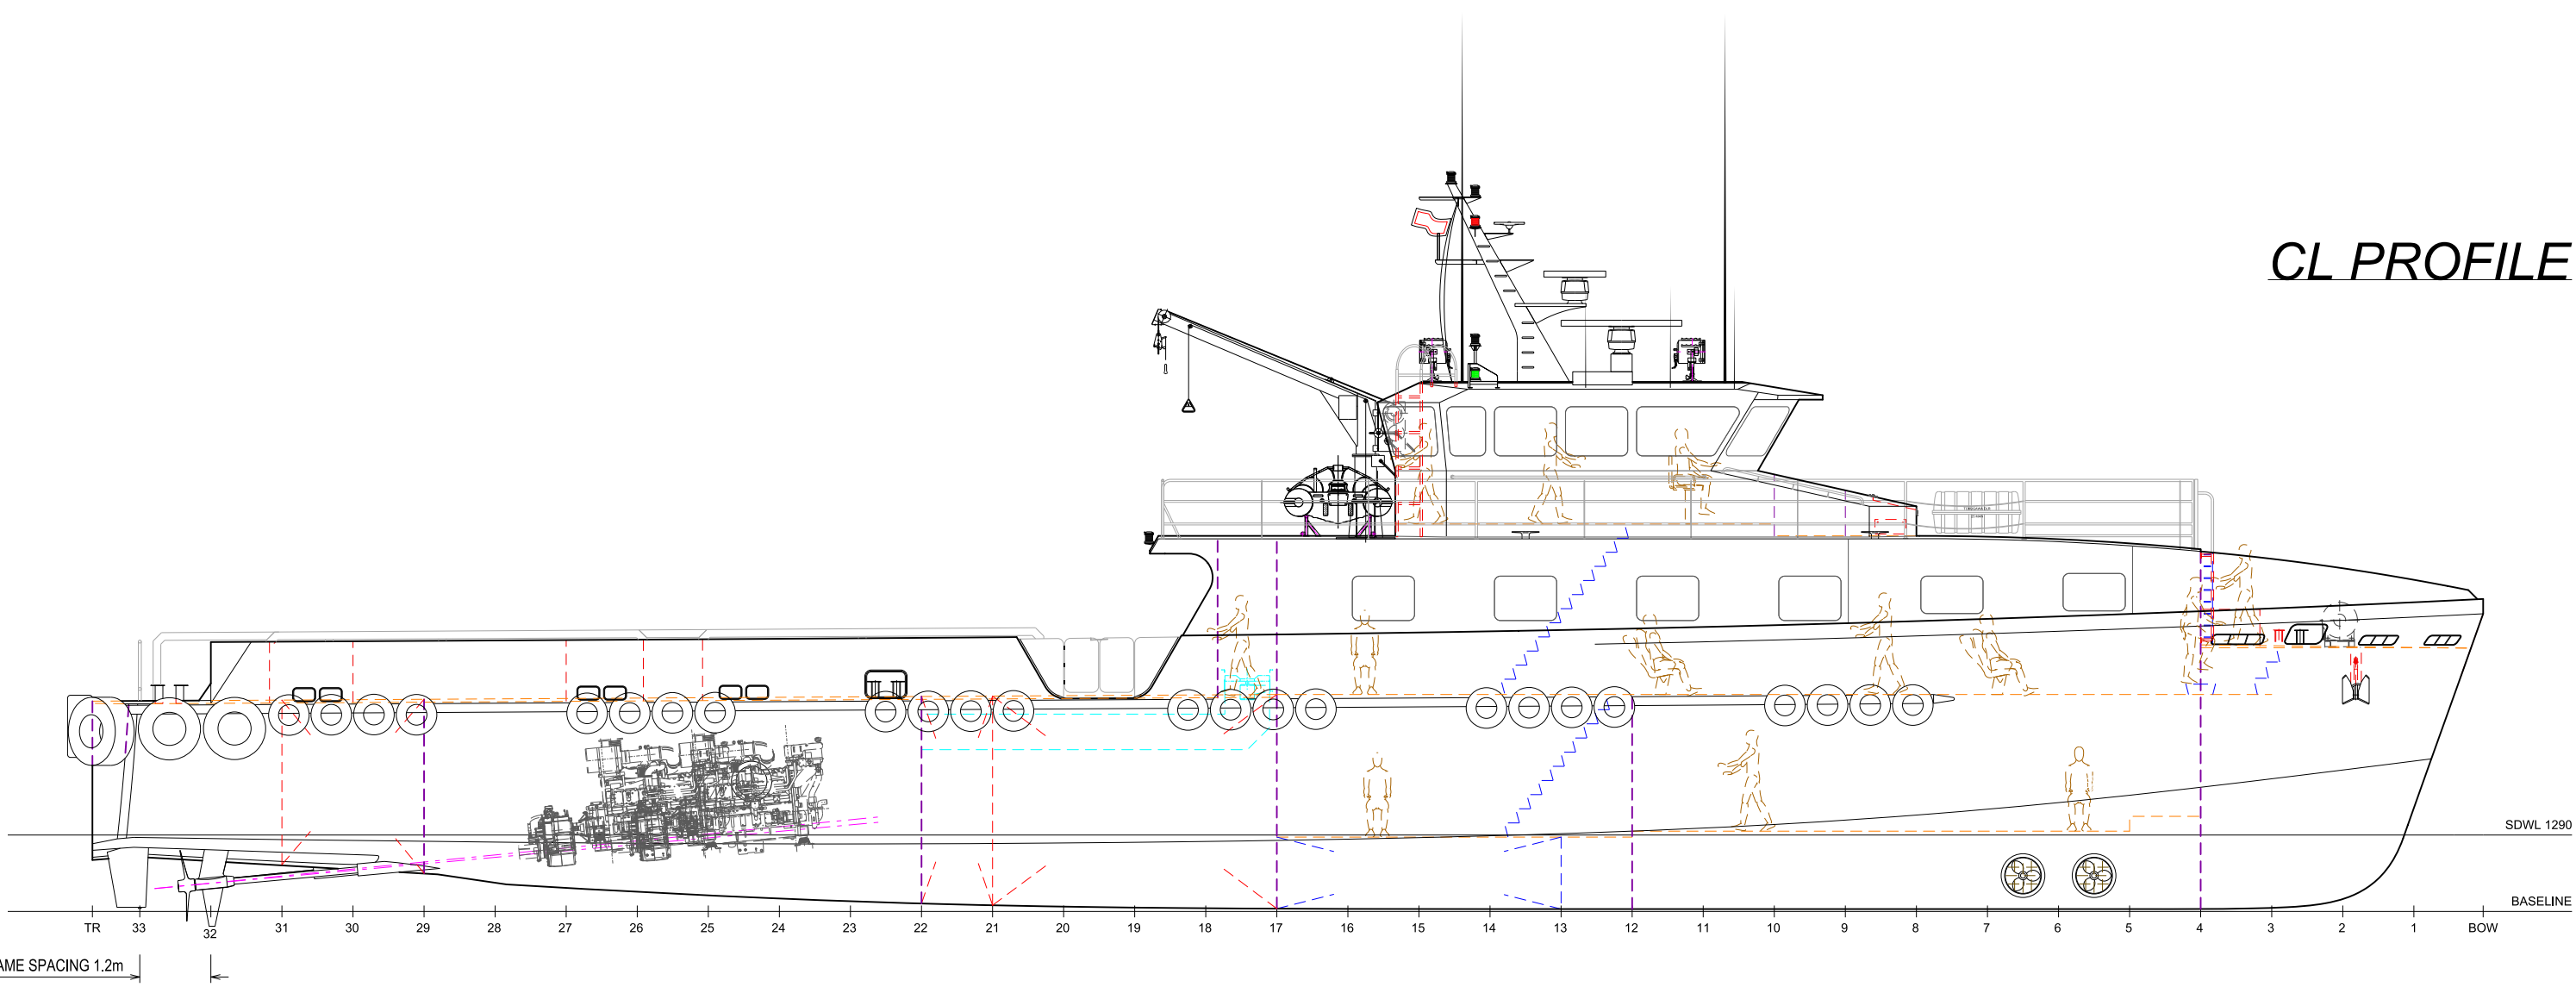
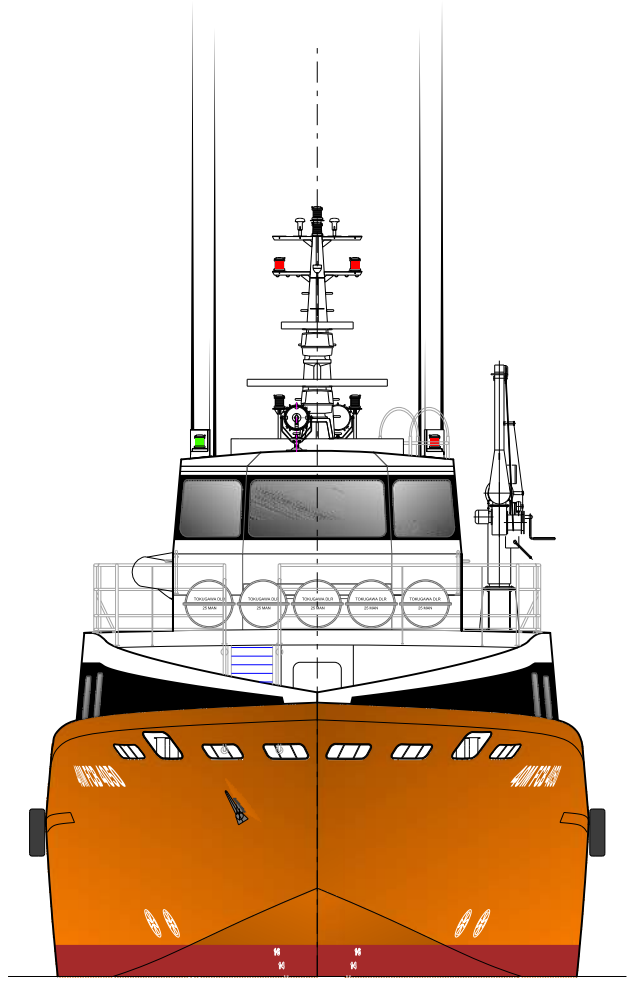


CL PROFILE

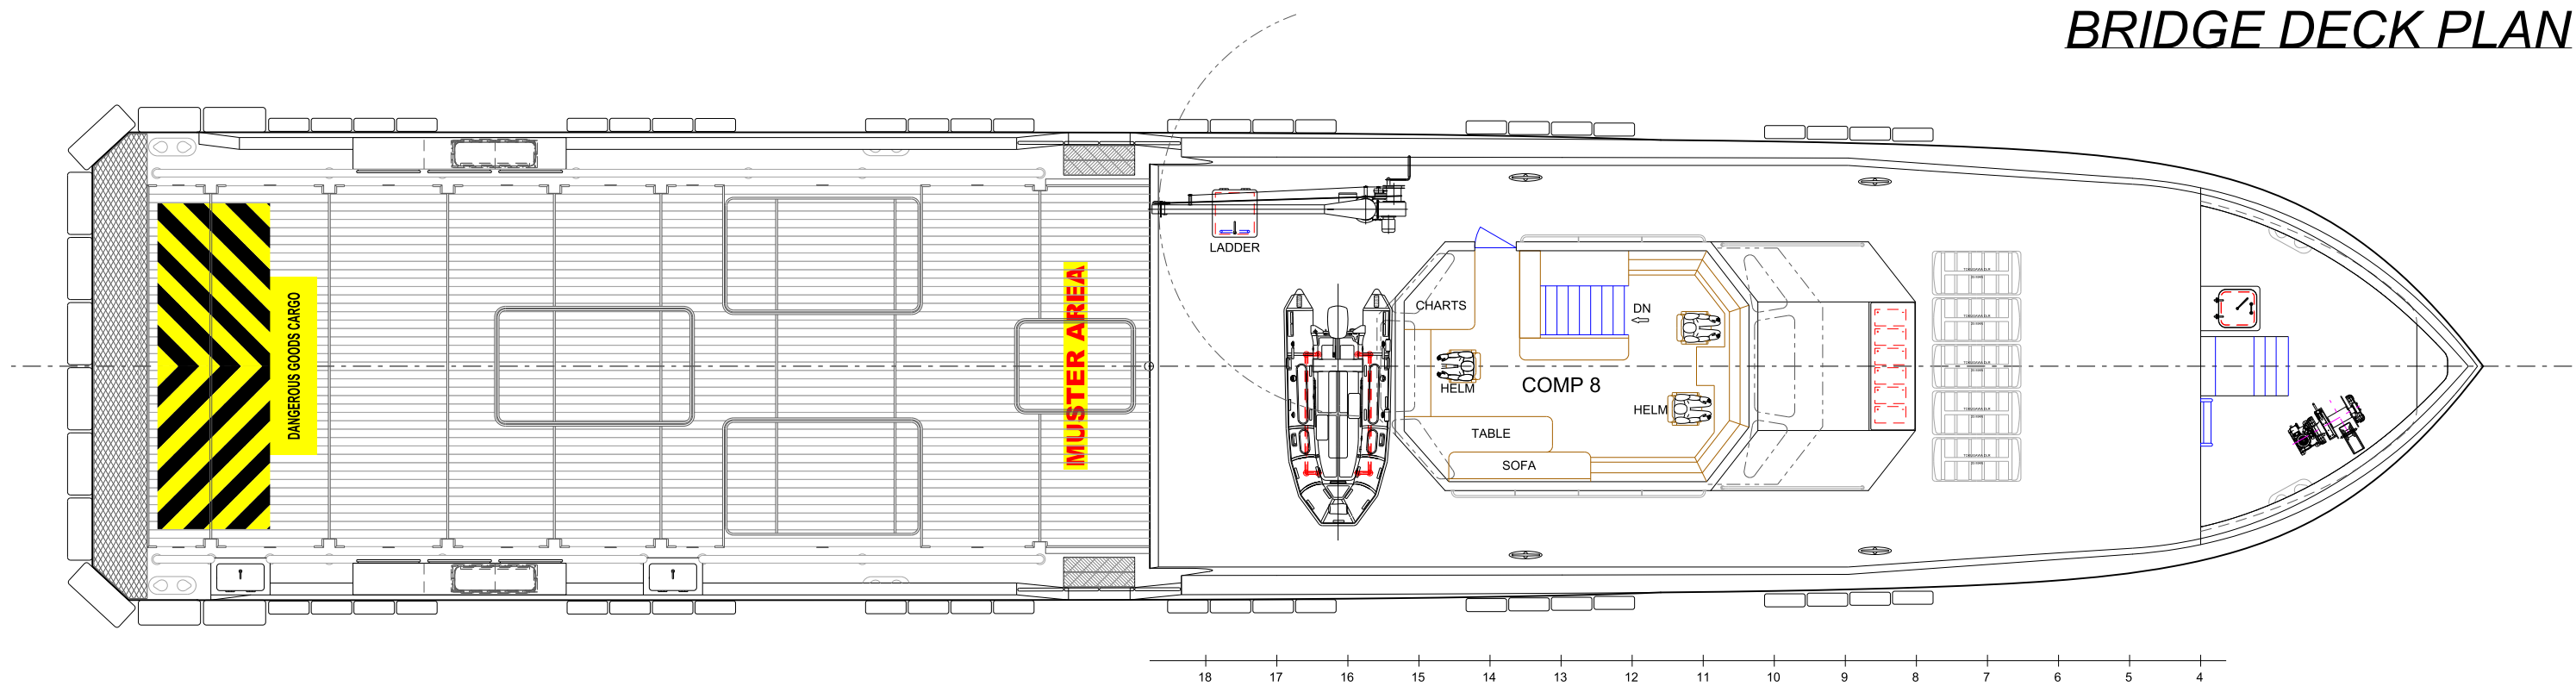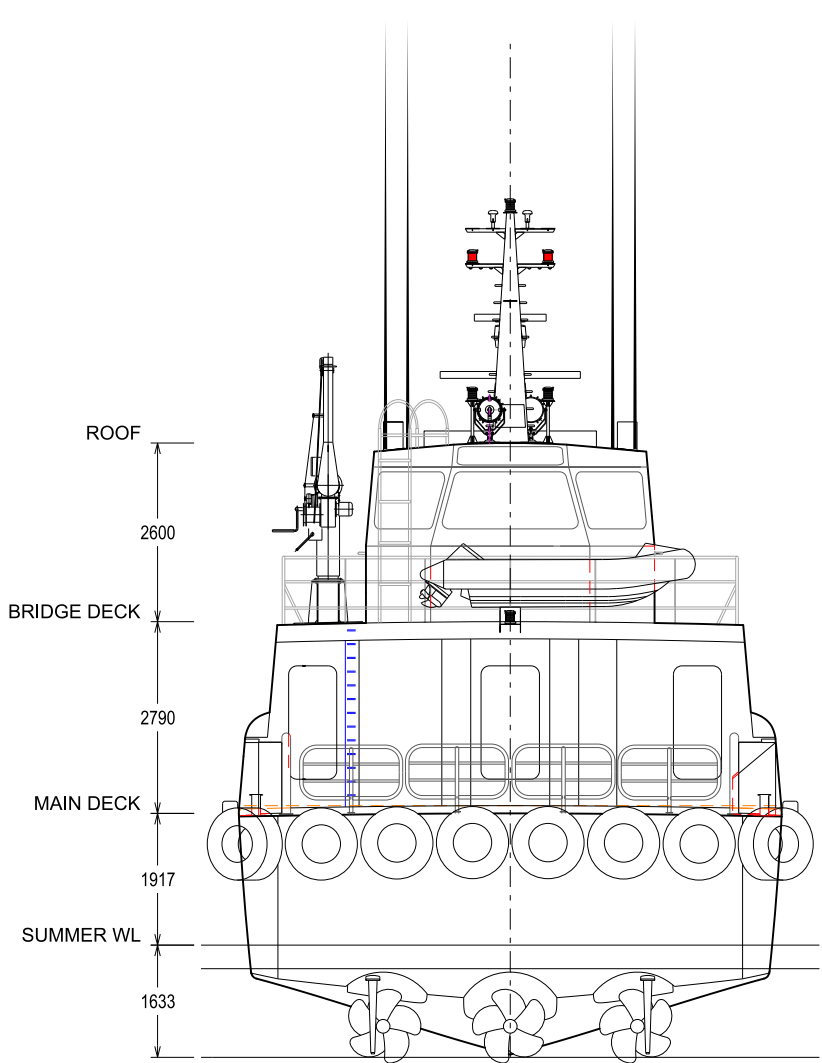


BRIDGE DECK PLAN

BOW BOARDING
OPTION

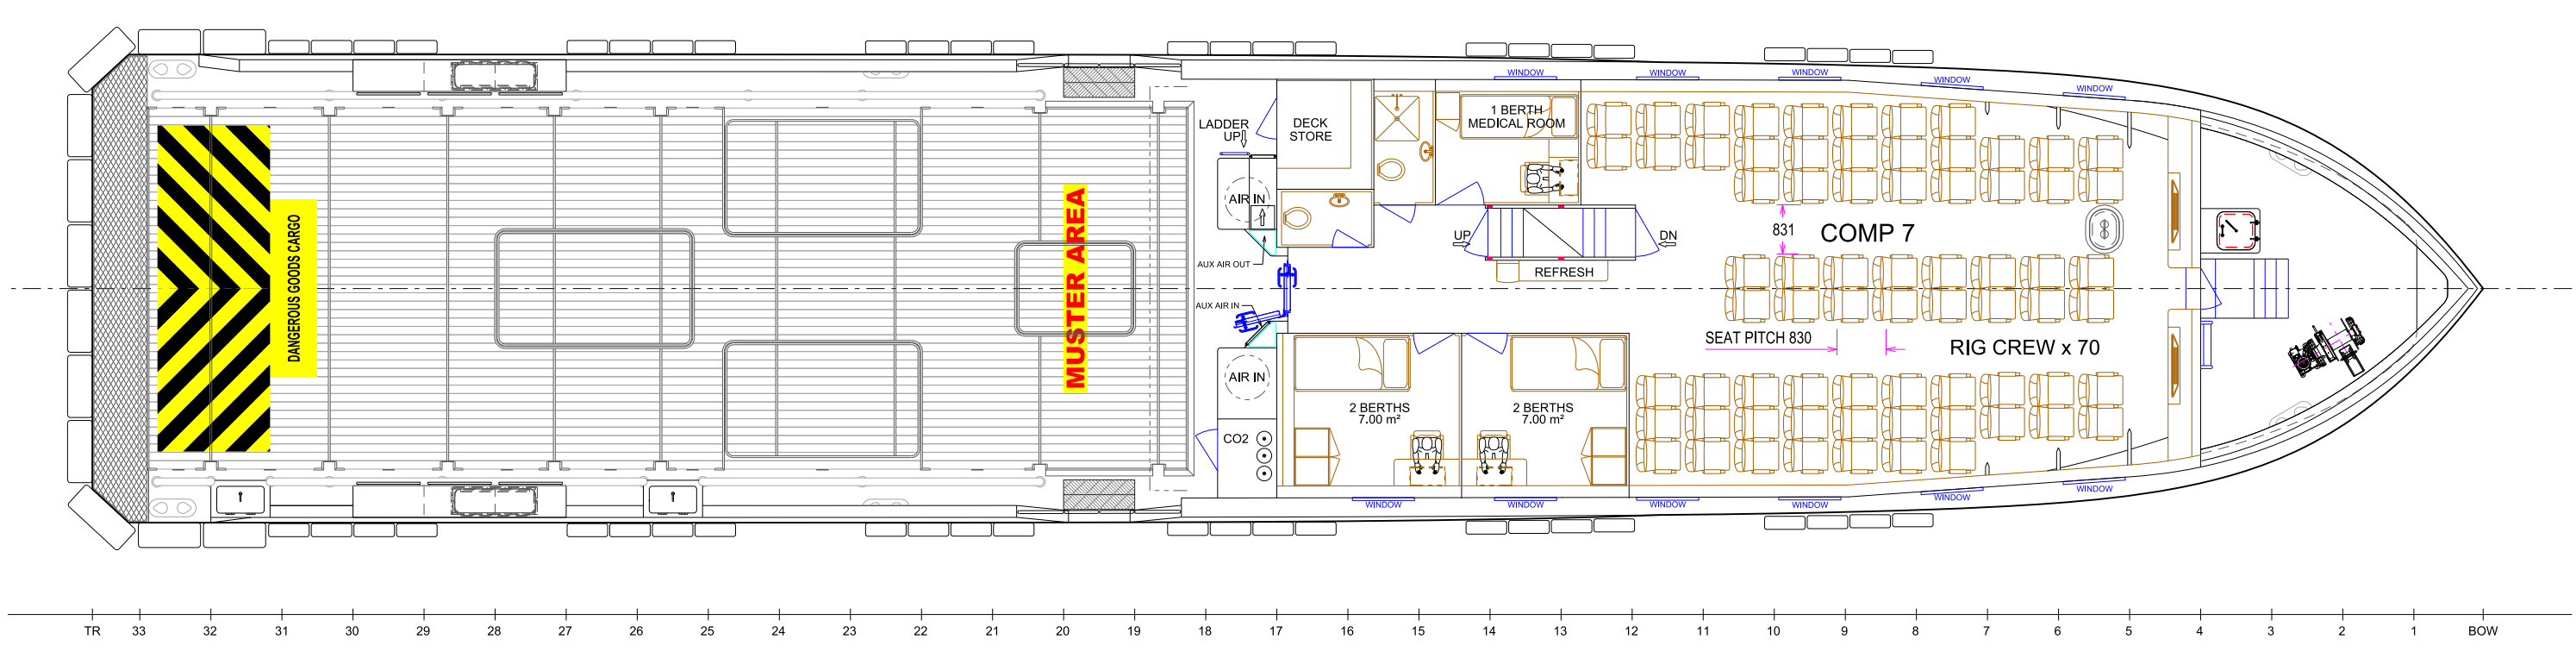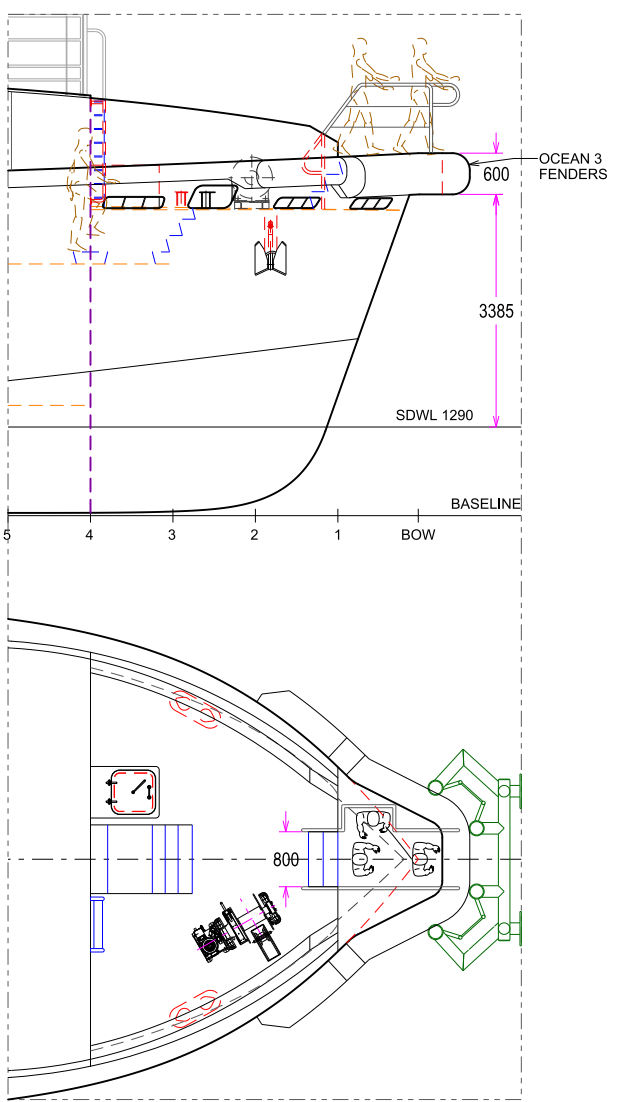

MAIN DECK PLAN

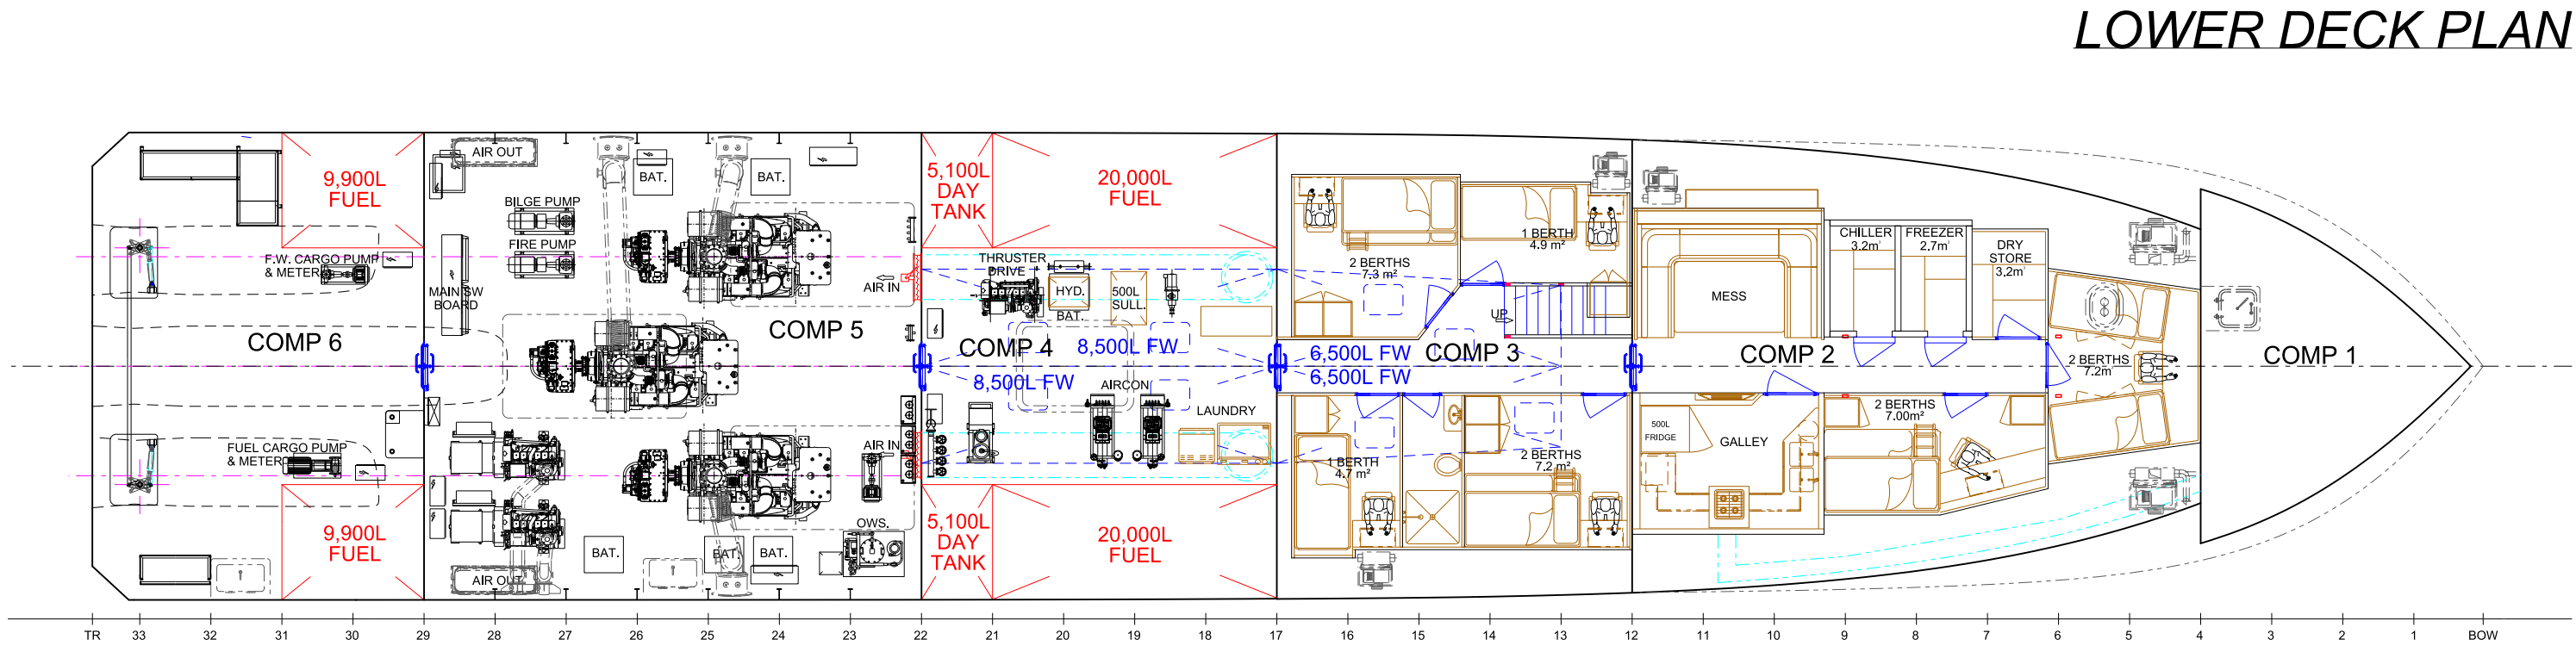

LOWER DECK PLAN

PRINCIPAL PARTICULARS		
LENGTH O.A.	m	40.4
BEAM MOULDED	m	7.9
DEPTH MOULDED	m	3.6
GRT		288
DRAFT. MAX BL	m	1.7
DRAFT. MAX PROP	m	1.9
CLEAR DECK	m'	120
FUEL OIL	m'	70
FRESH WATER	m'	30
BLACK WATER	m'	0.5
PASSENGERS		70
CABINS / BERTHS		8 / 14
DECK STRENGTH	t/m'	2.0
MAX DEAD WEIGHT	t	105
PROPULSION	bhp	4050
BOW THRUSTER	bhp	300
PRELIM. / PREDICTED SPEEDS		
AT 85% MCR, 50dwt	kts	25
AT 85% MCR, 40dwt	kts	26.5

PRELIMINARY
FOR REVIEW ONLY



Strategic Marine
LOT 5, CLARENCE BEACH ROAD
HENDERSON W.A. 6160
TELEPHONE (618) 94374840
FACSIMILE (618) 94374838

TITLE
GENERAL ARRANGEMENT

PROJECT
40M FAST CREW BOAT (FCB) 4050
DRAWING REF.
S799-110_A-D4

HULL NO.
TBC
SHEET NO.
1 OF 1
SCALE
1:110
OR AS SHOWN

DRAWN
M.BARNETT
CHECKED
A.TAYLOR
APPROVED
A.TAYLOR
DATE
30/04/2014

THIS DRAWING AND ALL INFORMATION CONTAINED WITHIN REMAIN THE SOLE PROPERTY OF SOUTHERLY DESIGNS PTY LTD NO PART MAY BE COPIED, MODIFIED OR REPRODUCED IN ANY MANNER WITHOUT THE PRIOR PERMISSION OF SOUTHERLY DESIGNS PTY LTD.

SHEET SIZE
A1

A-D4	FWD ACCOMMODATION MODIFIED, REFRIGERATED STORES ADDED	06/08/2014	A.TAYLOR	A.TAYLOR	A.TAYLOR
A-D3	PRINCIPAL PARTICULARS UPDATED, 2ND BOW THRUSTER ADDED WT DOORS UPDATED	08/07/2014	M.BARNETT	A.TAYLOR	A.TAYLOR
A-D2	DECK CRANE & FIJI REMOVED	07/07/2014	M.BARNETT	A.TAYLOR	A.TAYLOR
A-D1	LOWER DECK DRY STORE AND ACCOM REVISED	04/07/2014	L.PORTUGUEZ	G.DANIEL	G.DANIEL
REV	REVISION DETAILS	DATE	DRN	CHECKED	APPROVED