

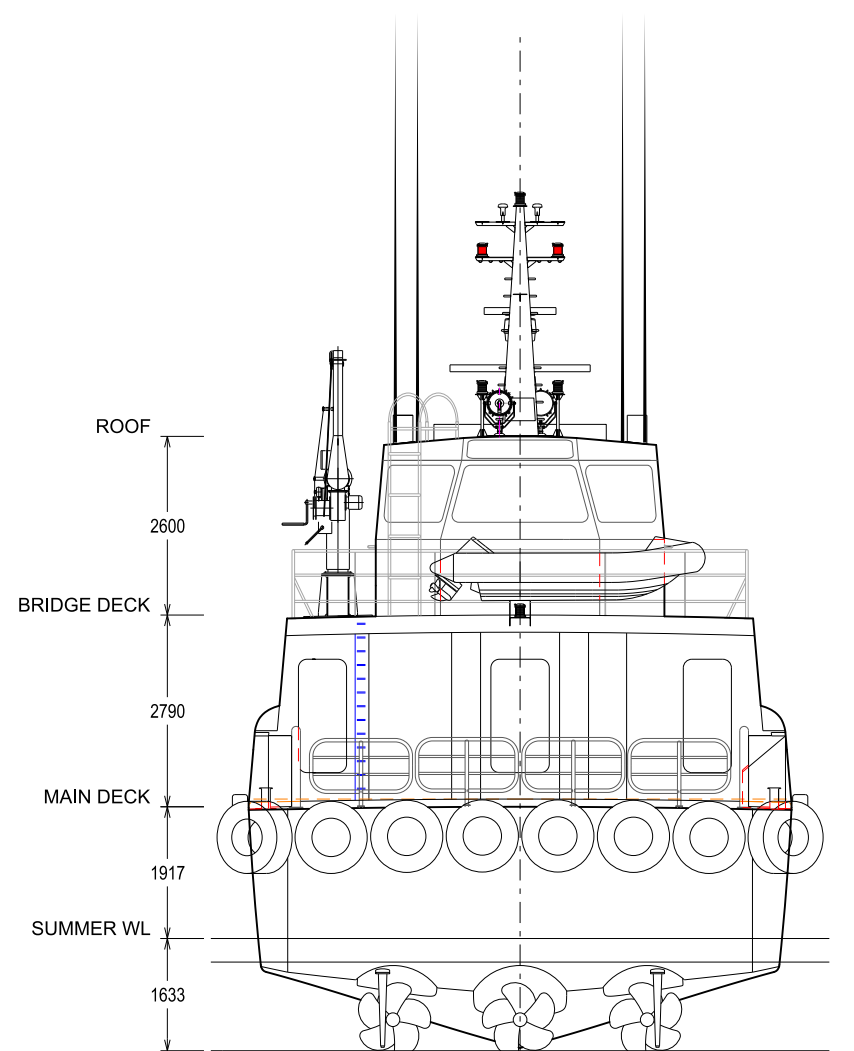
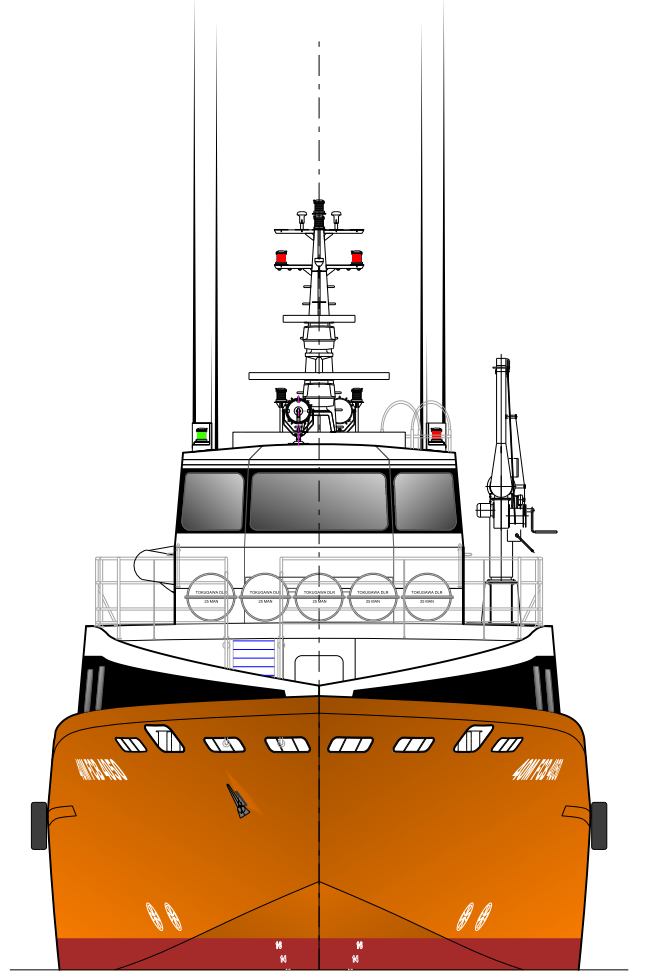
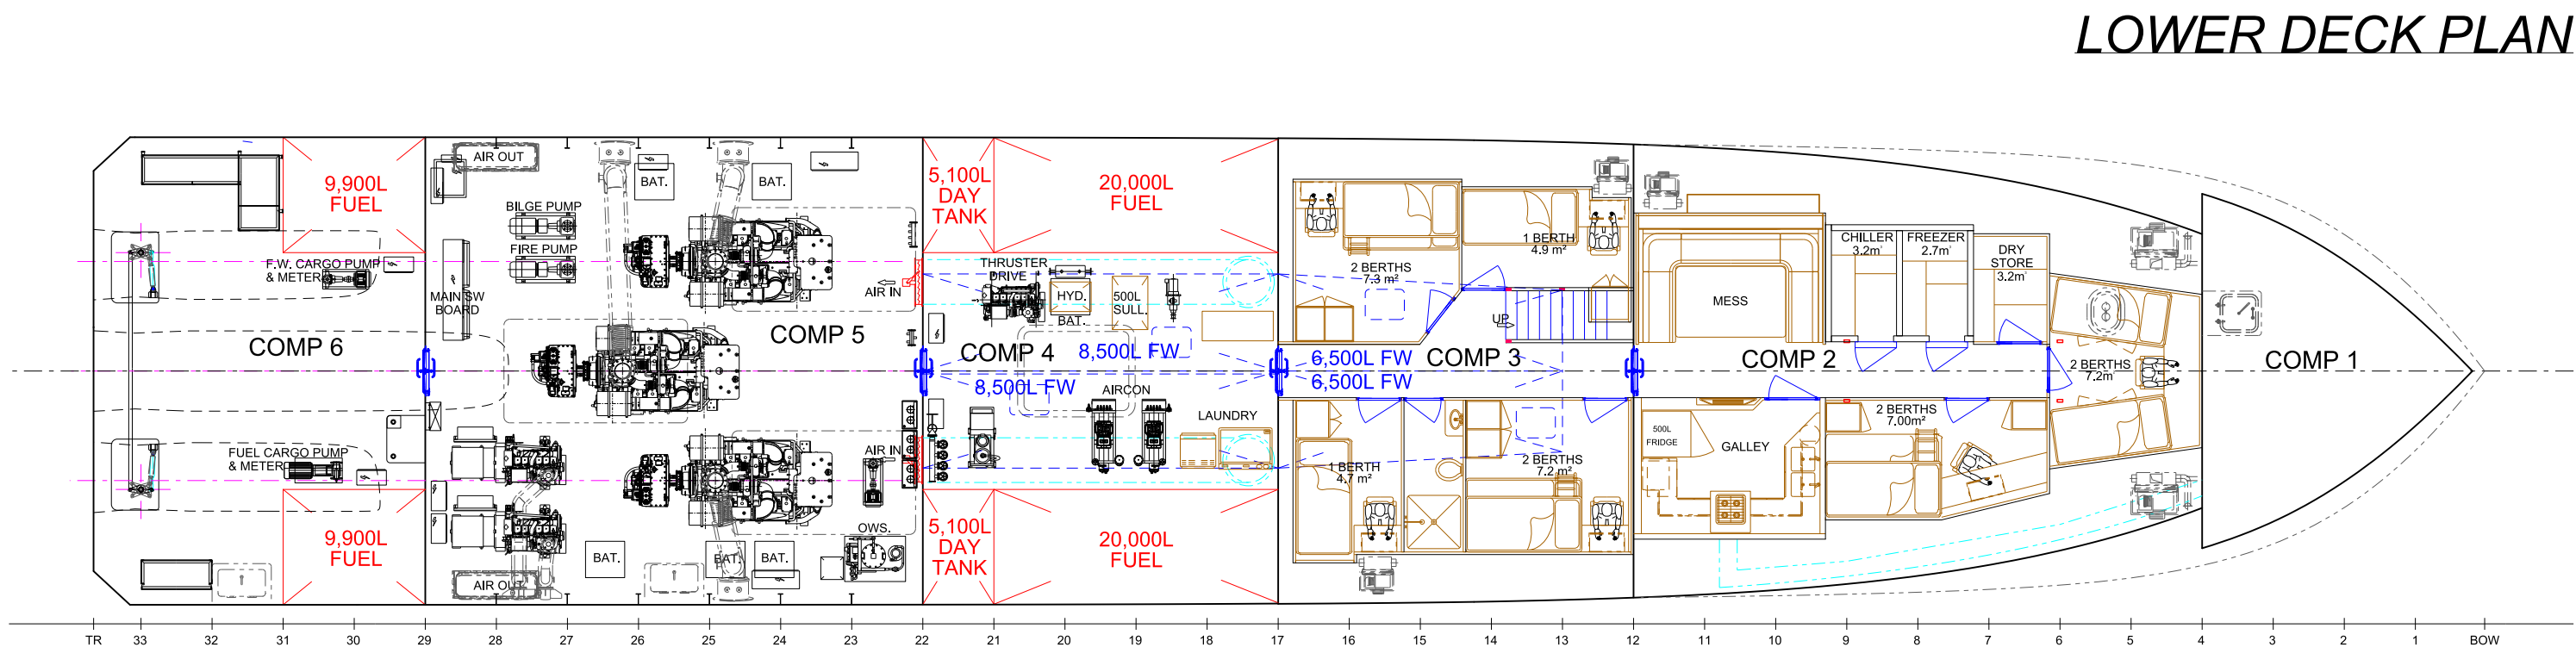
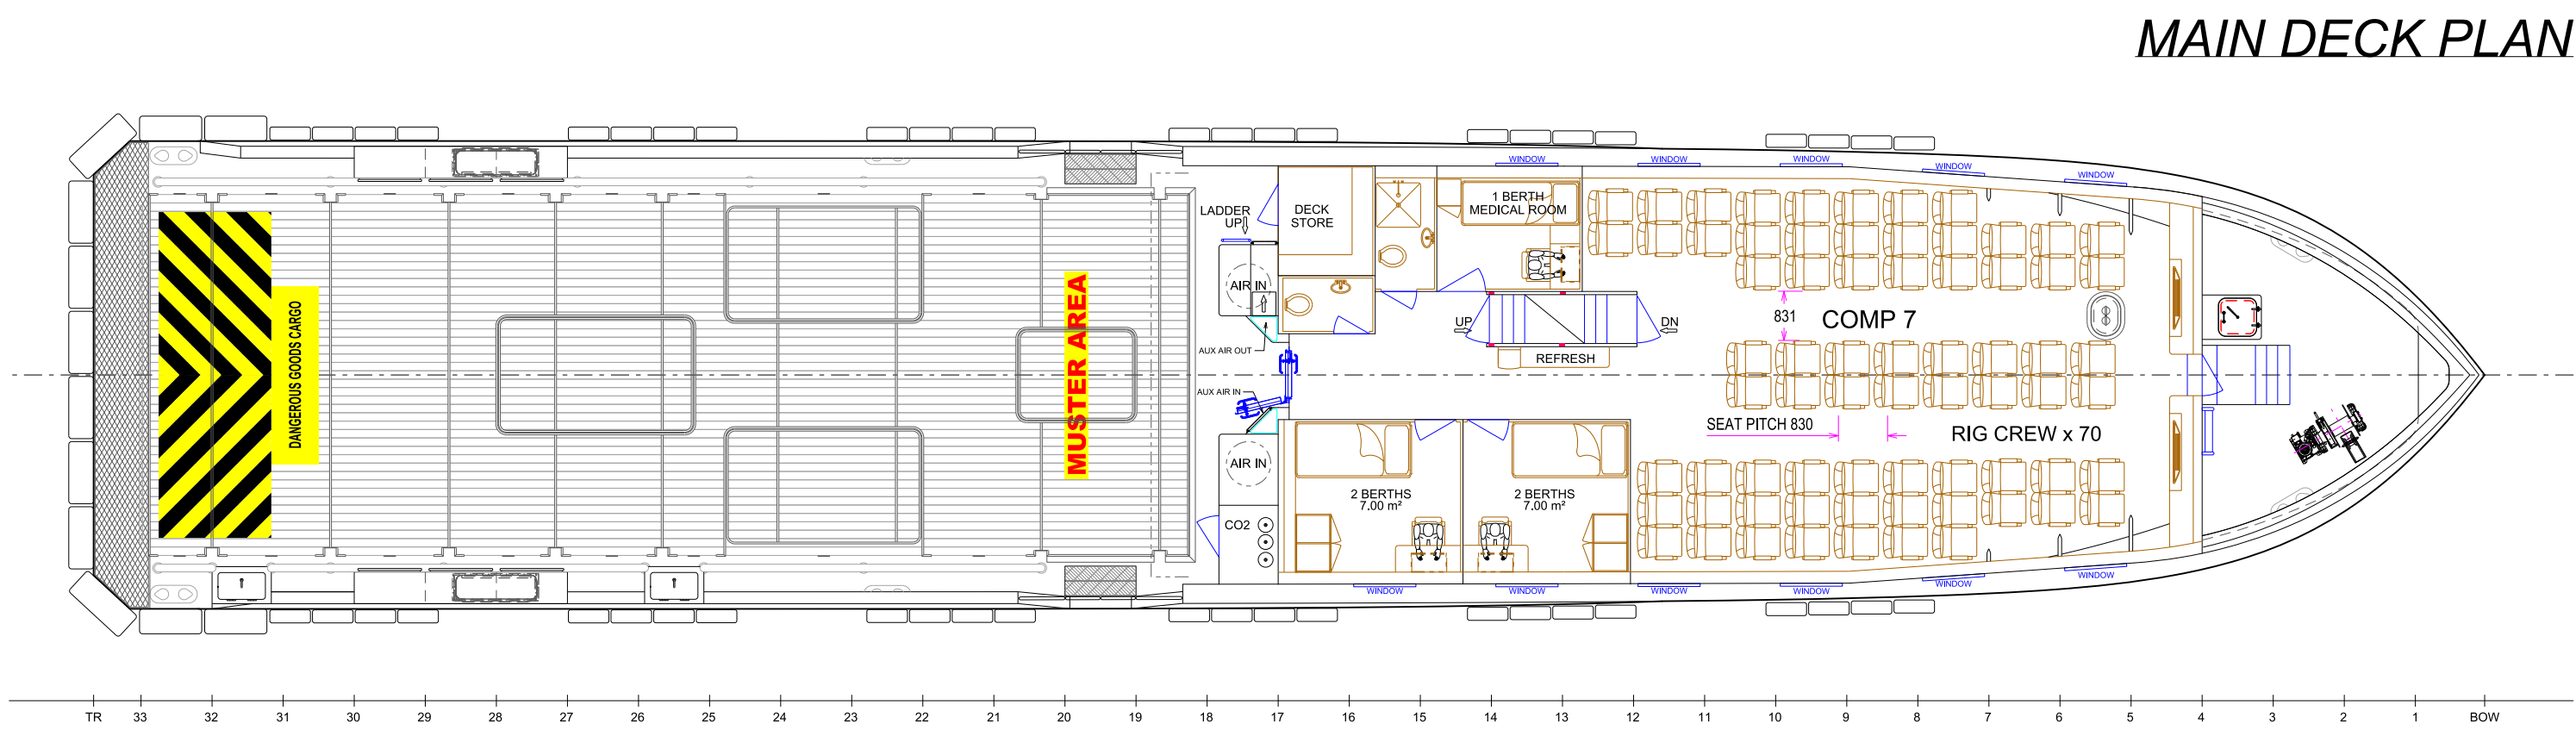
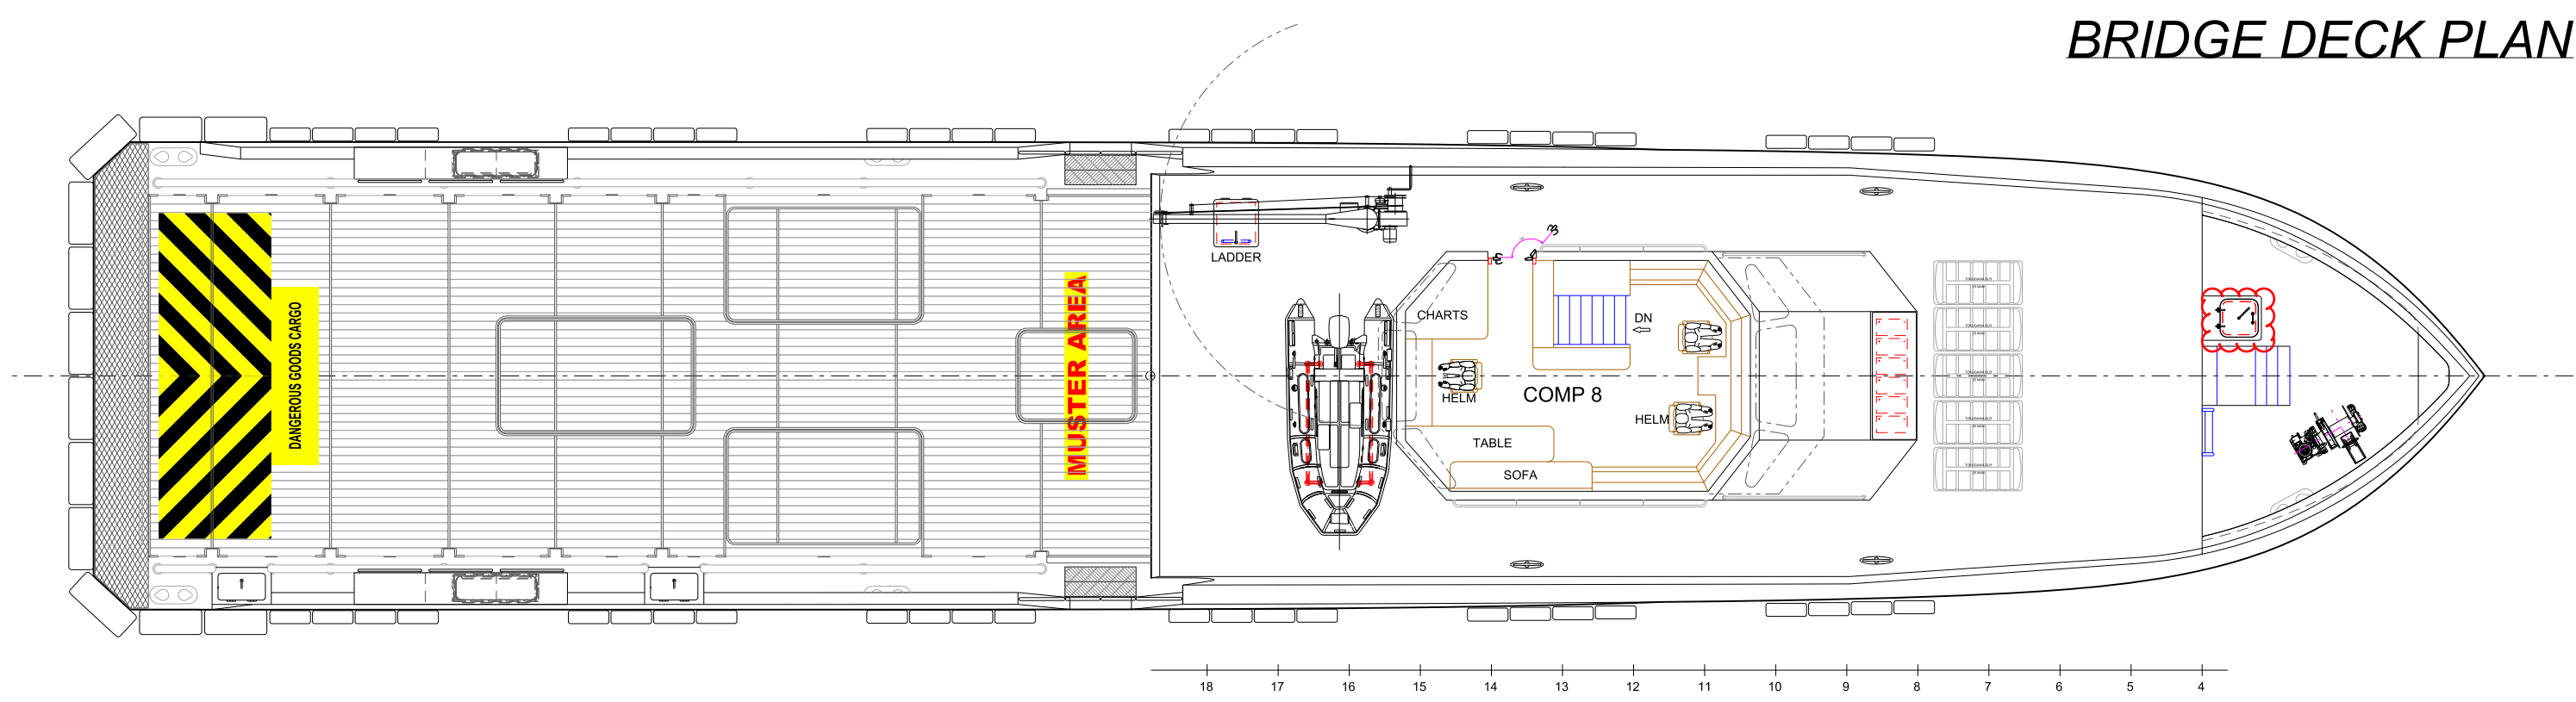
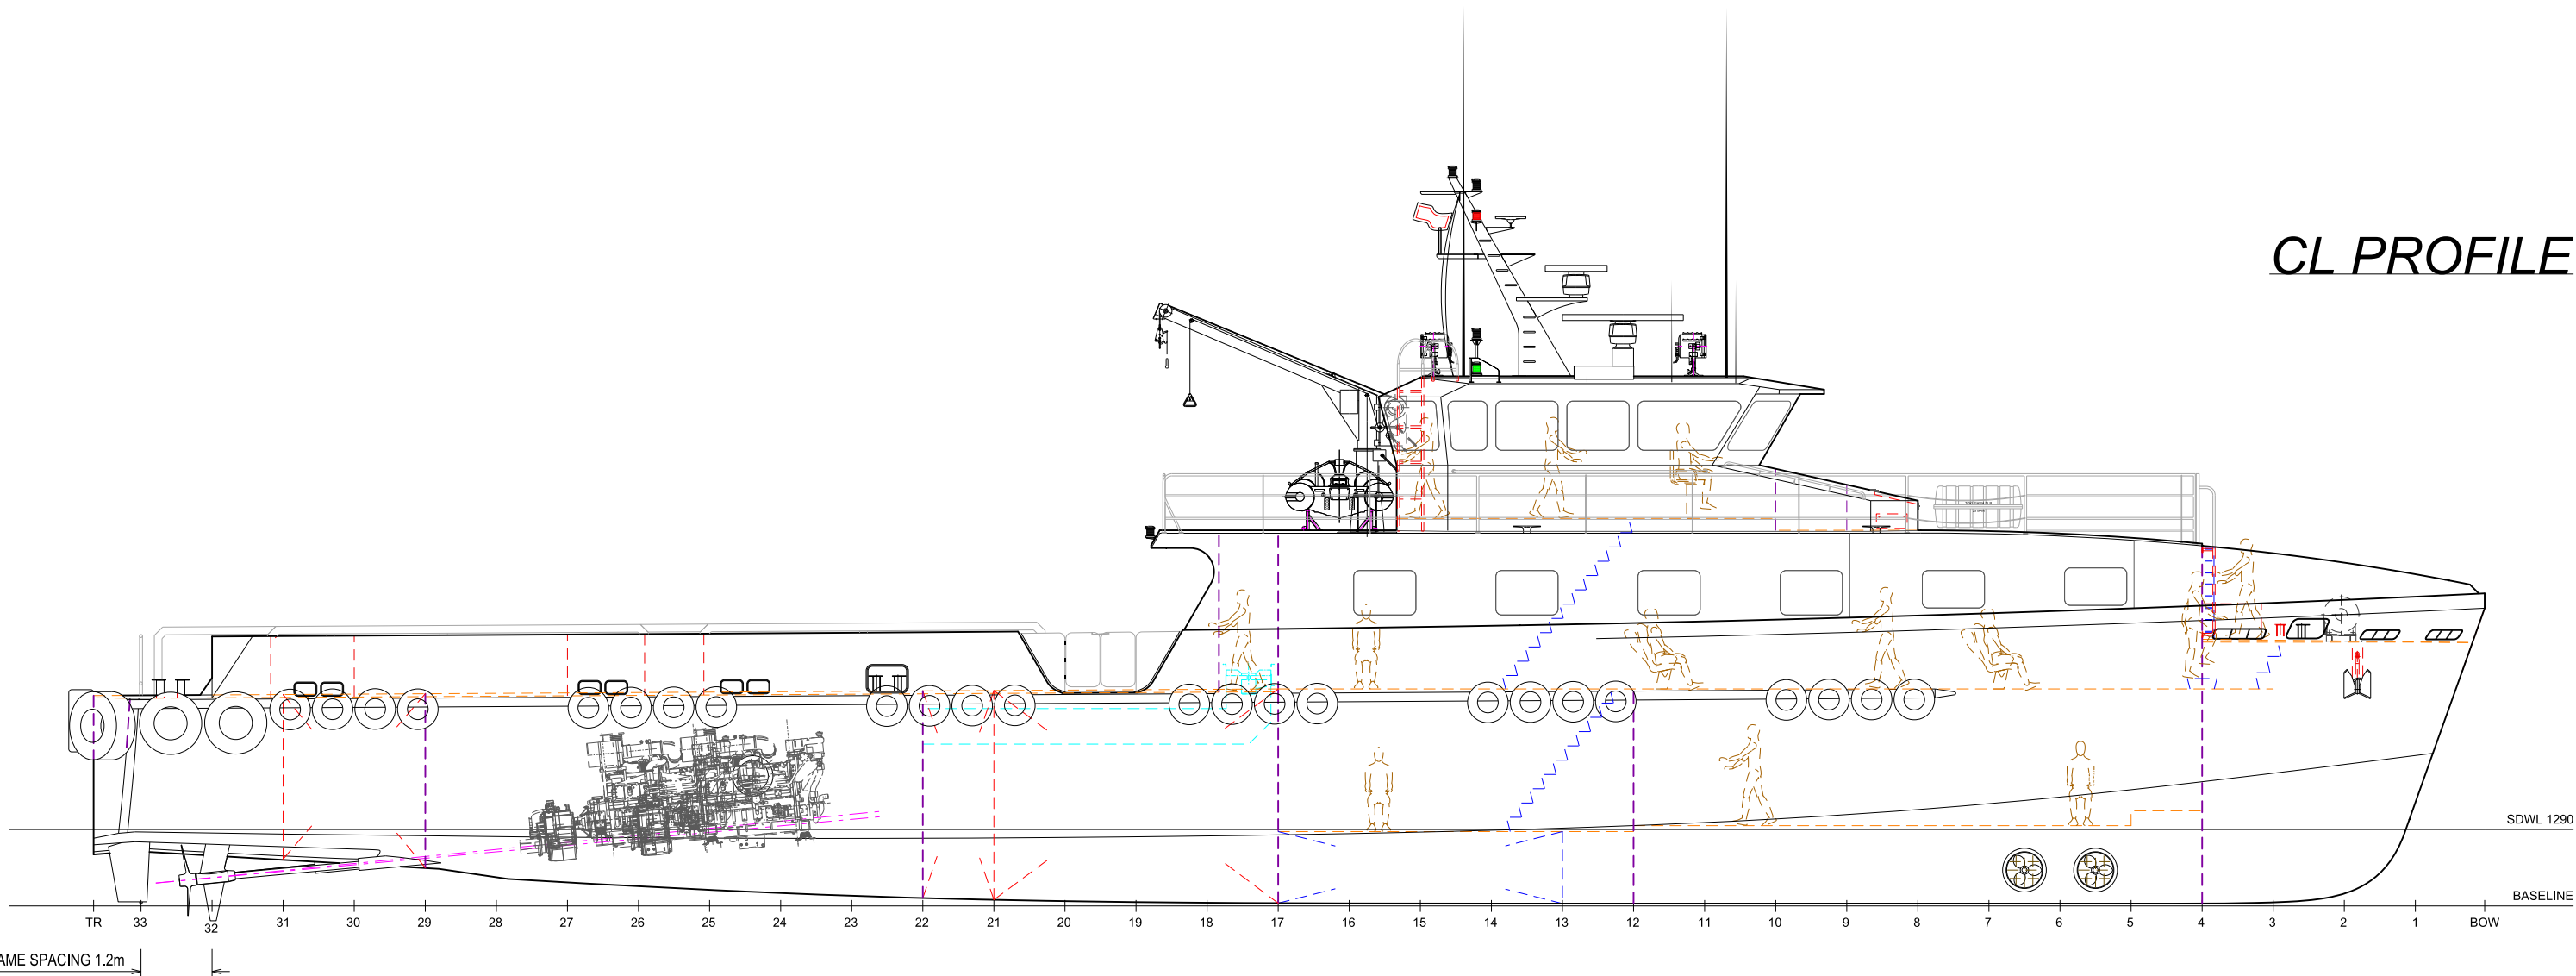


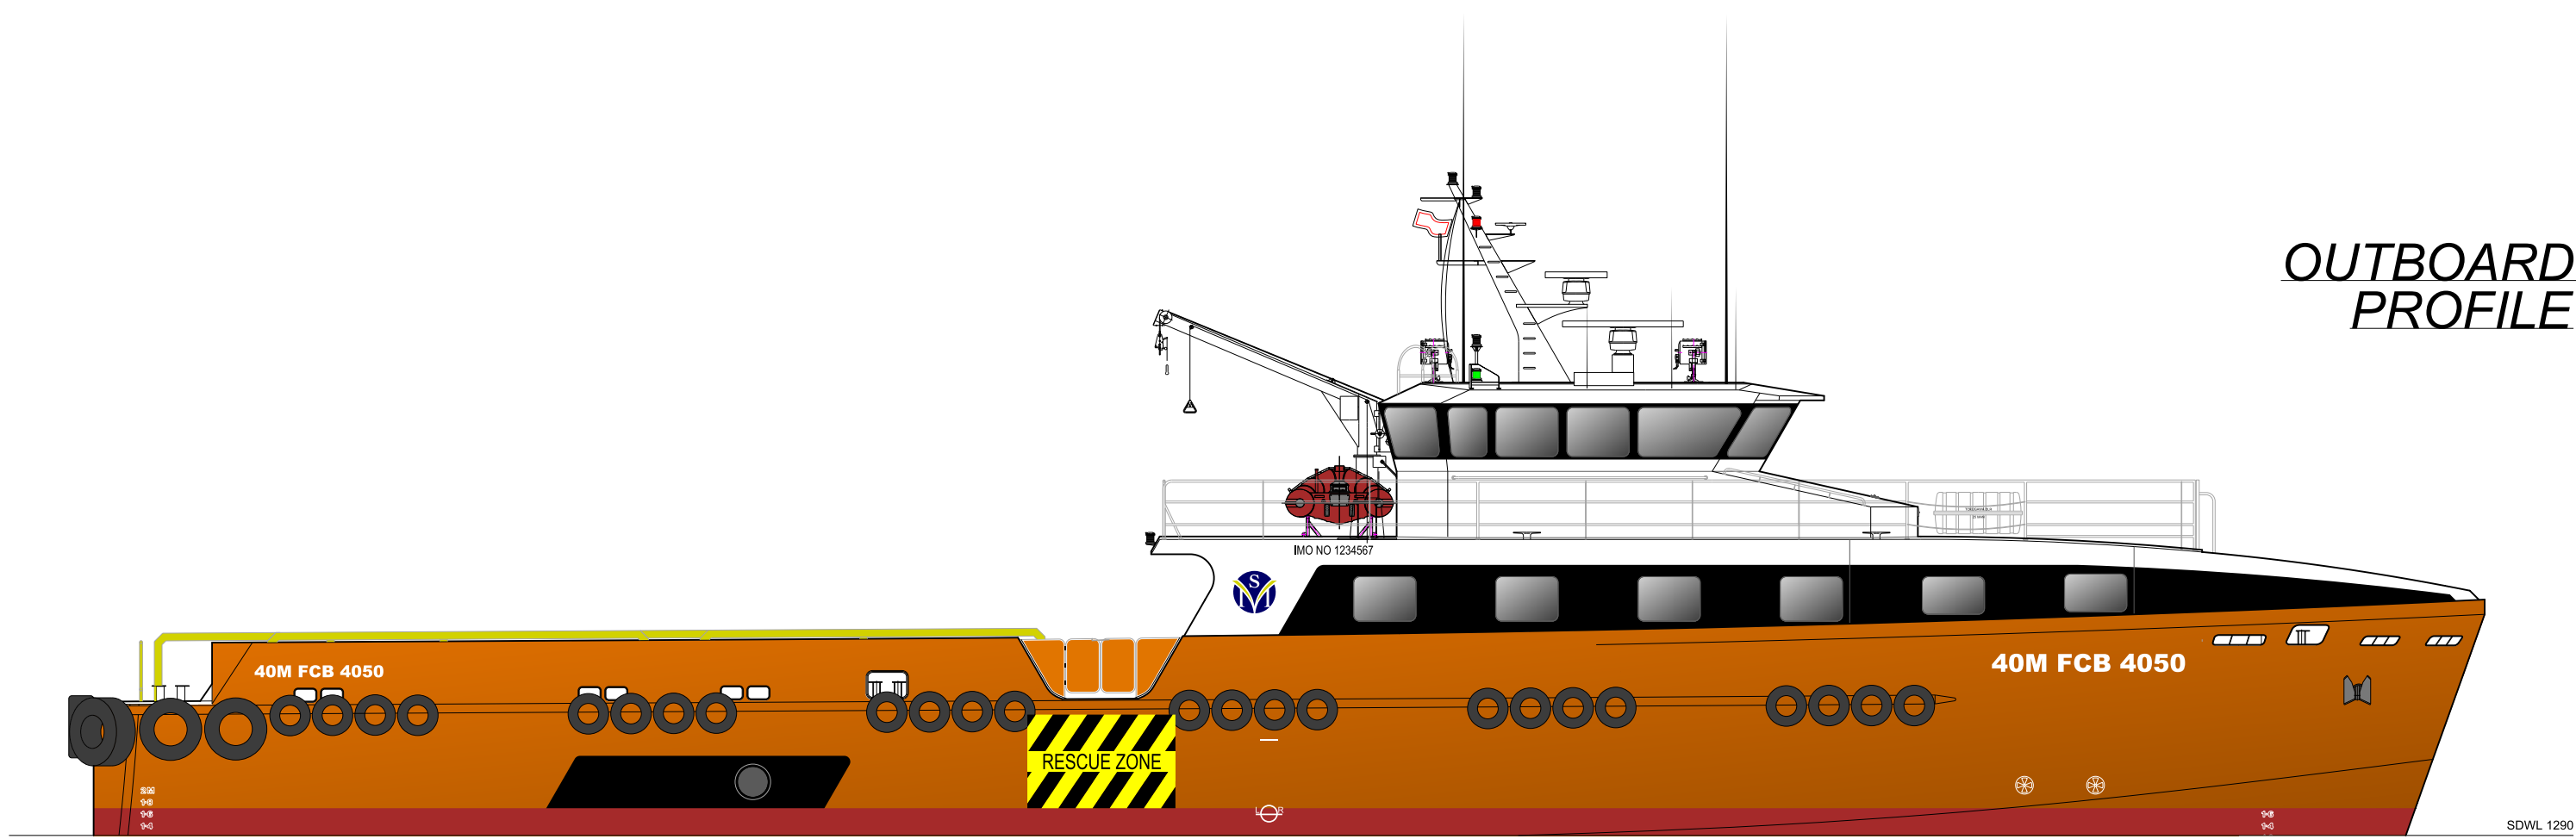

BOW BOARDING OPTION

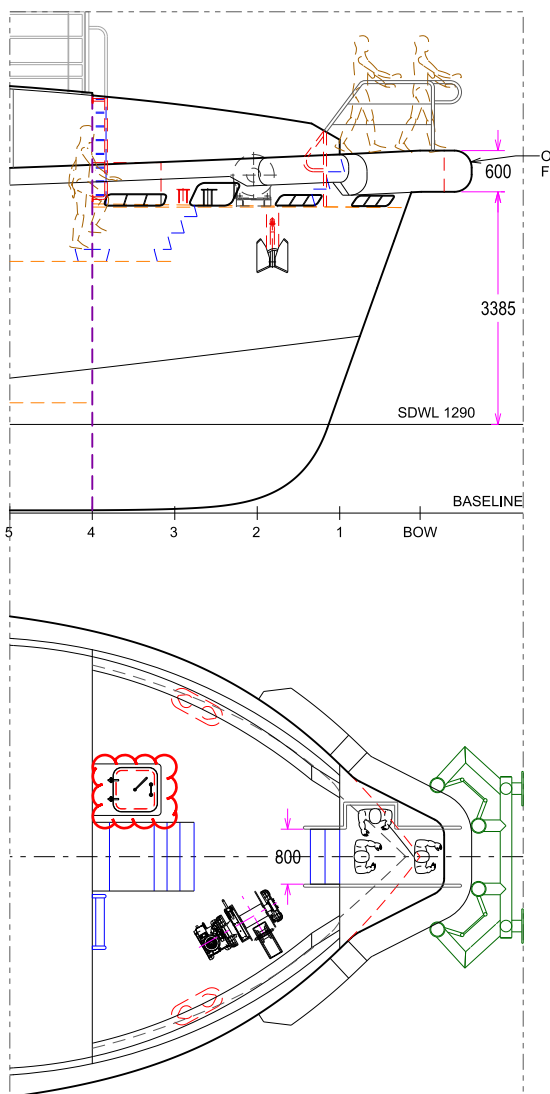

PRINCIPAL PARTICULARS		
LENGTH O.A.	m	40.4
BEAM MOULDED	m	7.9
DEPTH MOULDED	m	3.6
GRT		288
DRAFT: MAX BL	m	1.7
DRAFT: MAX PROP	m	1.9
CLEAR DECK	m	120
FUEL OIL	m ³	70
FRESH WATER	m ³	30
BLACK WATER	m ³	0.5
PASSENGERS		70
CABINS / BERTHS	8 / 14	
DECK STRENGTH	t/m ²	2.0
MAX DEAD WEIGHT	t	105
PROPULSION	bhp	4050
BOW THRUSTER	bhp	300
PRELIM. / PREDICTED SPEEDS		
AT 85% MCR, 50dwt	kts	25
AT 85% MCR, 40dwt	kts	26.5

FOR CONSTRUCTION

FOR INFORMATION ONLY
Retained as supporting
documentation



EXAMINED
This plan has been examined and given the
status as shown in the Design Appraisal
Document (DAD) number below
SATS/HULL/0013055
Date: 06 November 2024 Initials: ST
Marine, South Asia Technical Support Office
Lloyd's Register Asia



LOT 5, CLARENCE BEACH ROAD
HENDERSON W.A. 6166
TELEPHONE (618) 94374860
FACSIMILE (618) 94374858

GENERAL ARRANGEMENT

PROJECT	40M FAST CREW BOAT (FCB) 4050	HULL NO.	194,195,398
DRAWING REF.	S799-15_001_B	SHEET NO.	1 OF 1
SCALE	1:110	SCALE	OR AS SHOWN
DATE	11/08/2014	SHEET SIZE	AI

B	BRIDGE DOOR SHIFTED, FW TANK MANHOLES UPDATED	14/08/2014	M.BARNETT	M.BARNETT	M.BARNETT
A	DJ'S MARKETING SERIES A FINALIZED ISSUED FOR PRODUCTION OF HULLS 194,195,398	11/08/2014	M.BARNETT	A.TAYLOR	A.TAYLOR
REV	REVISION DETAILS	DATE	DRN	CHECKED	APPROVED